



Teil 2

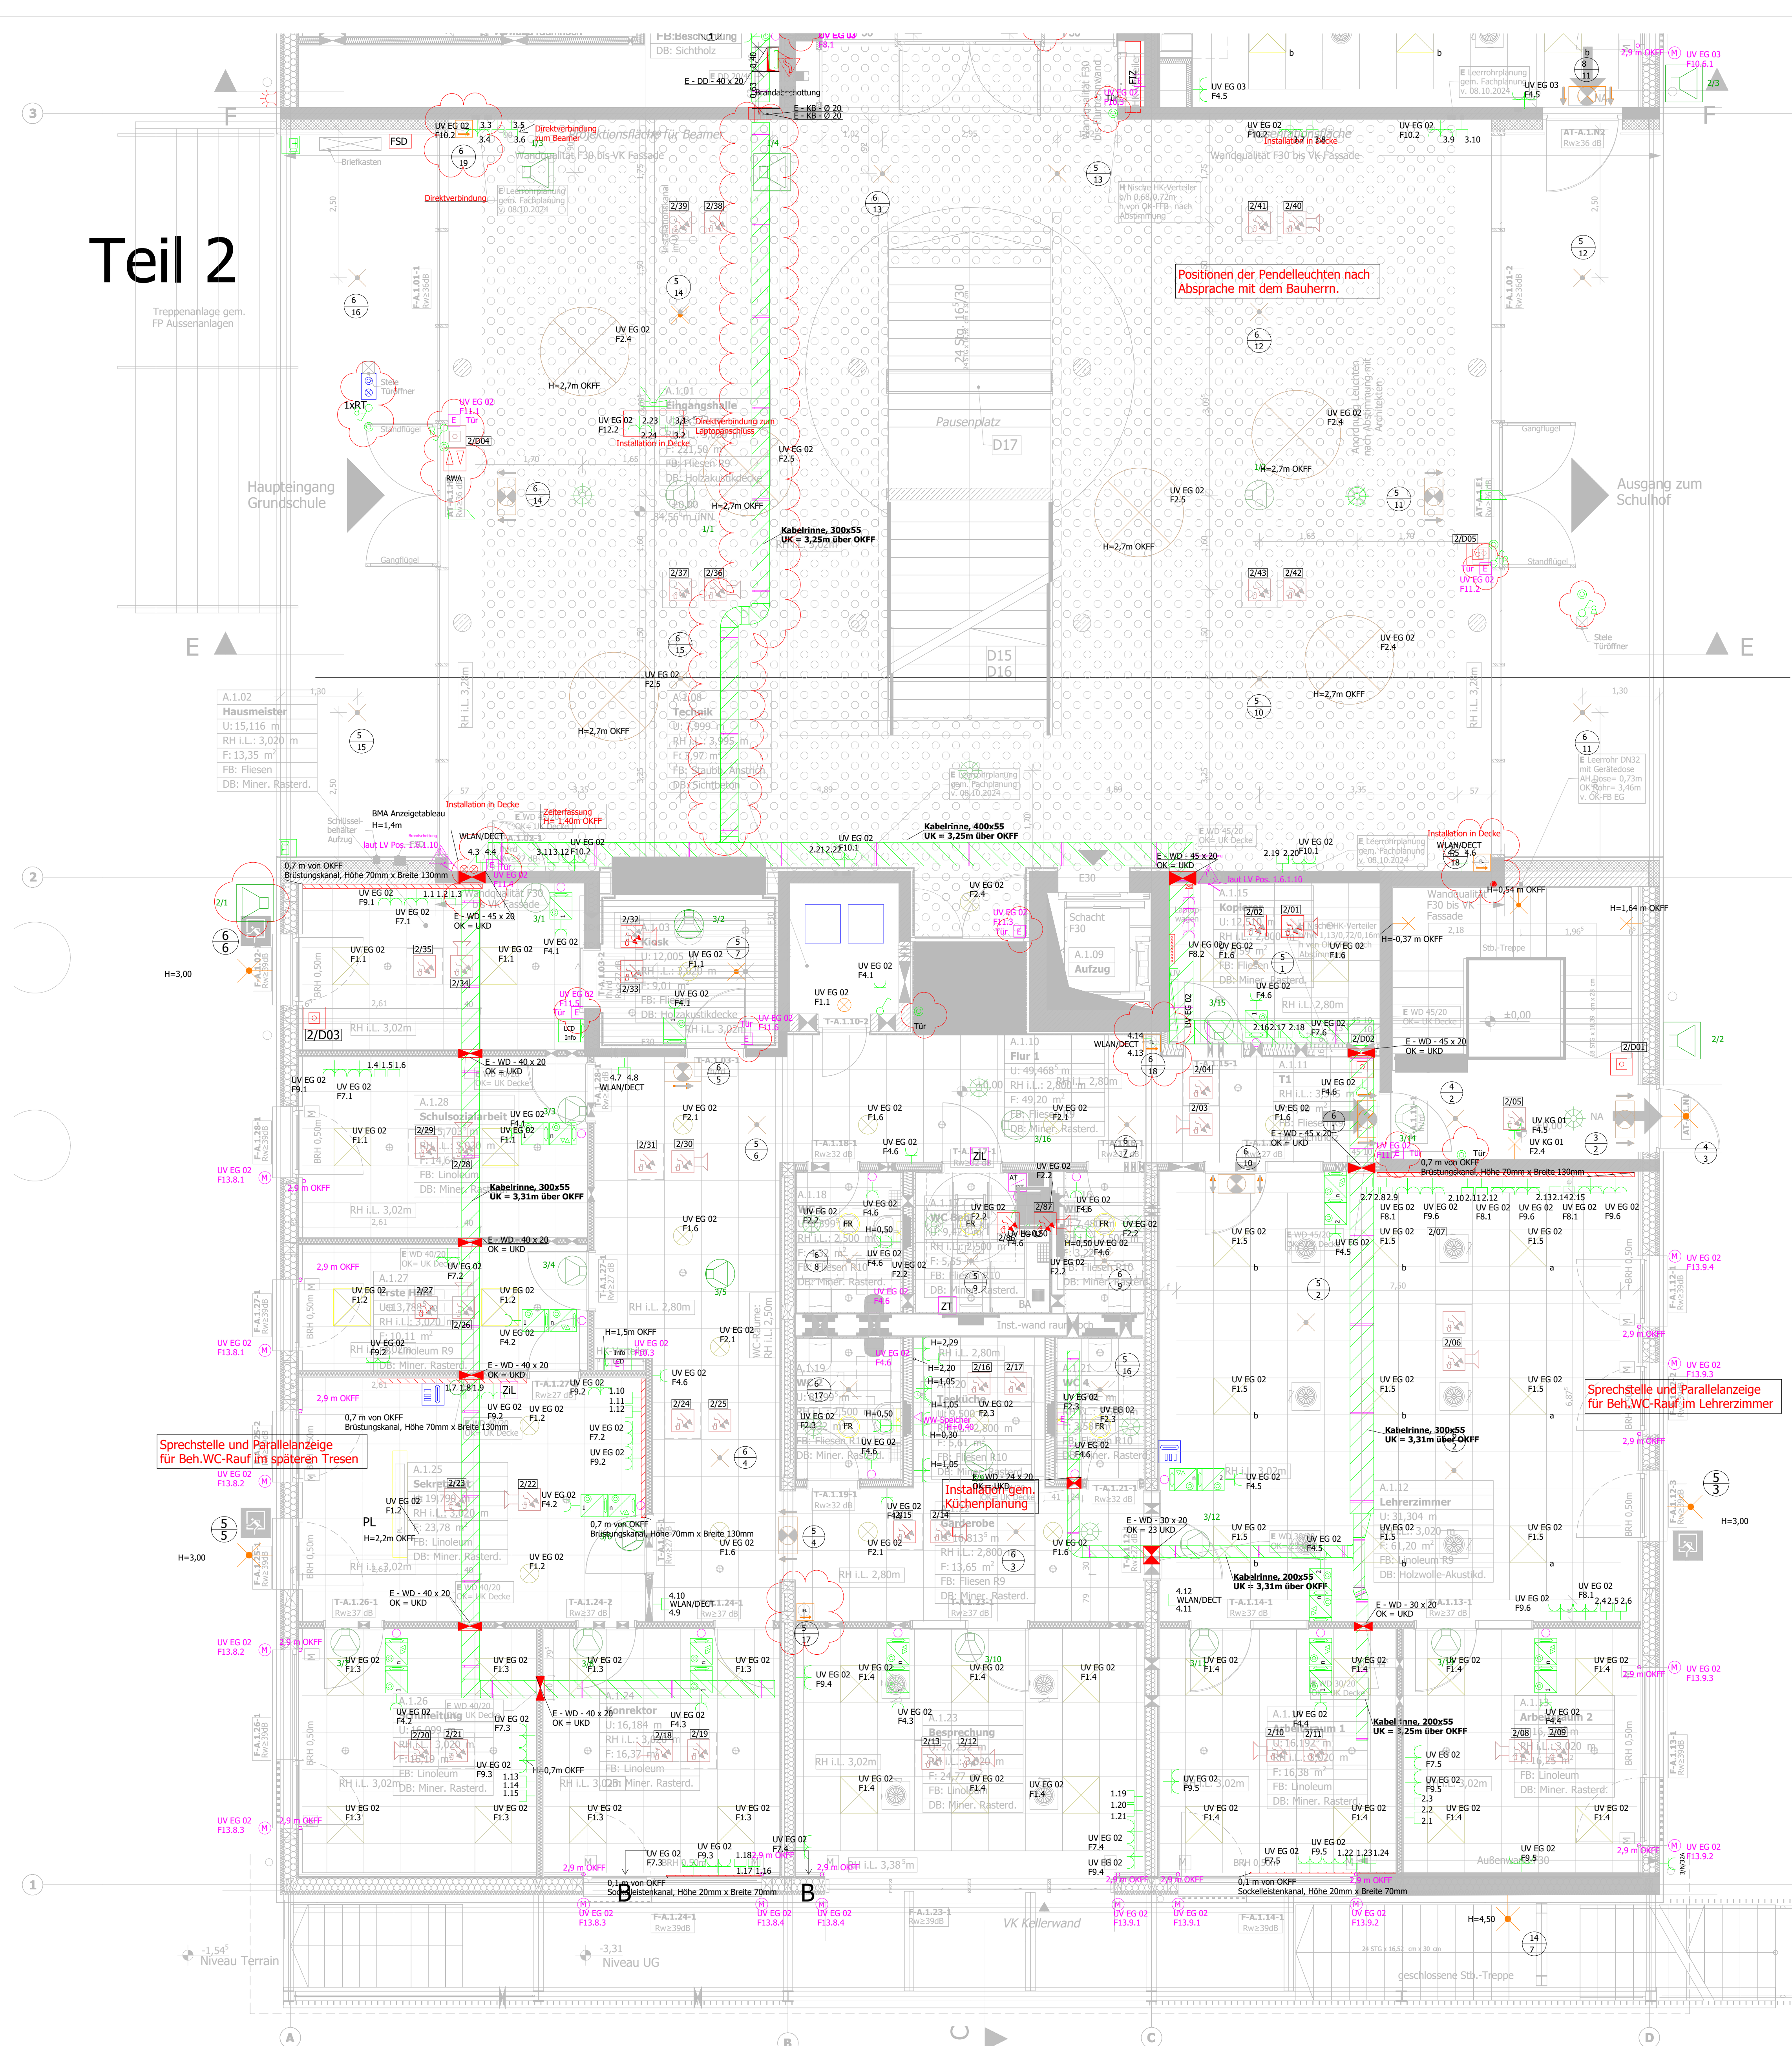

Teil 1

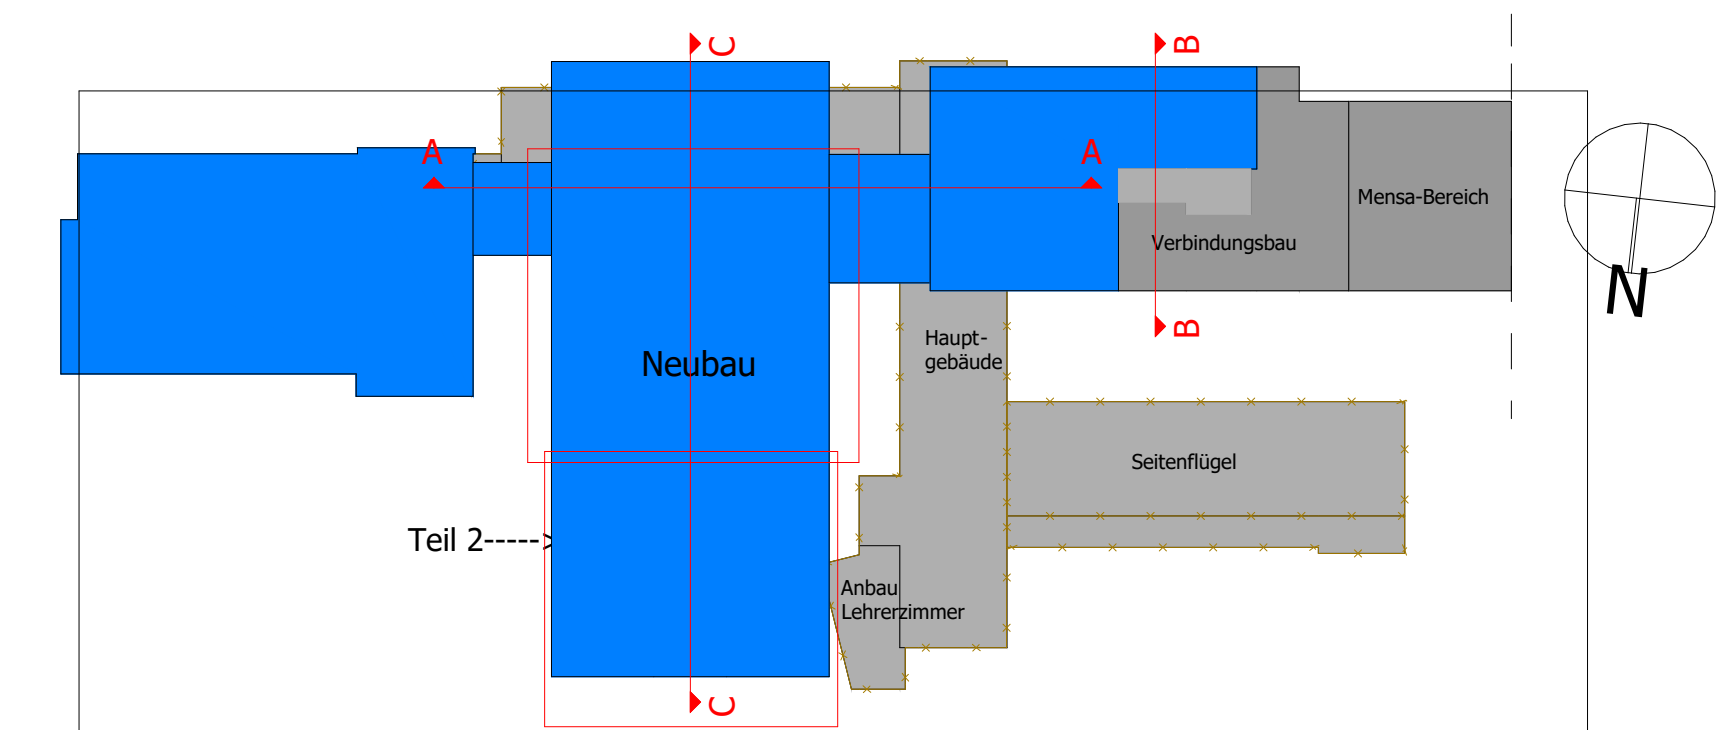

**Klassen und Gruppenräumen
Licht an über Taster**
- schaltet sanft ein auf 100%, Dauer 5 Sekunden
- Licht wird automatisch eingeschaltet
- Licht wird automatisch ausgeschaltet
Wird mindestens 10 Minuten keine Präsenz erkannt:
- schaltet der Präsenzmelder das Licht sanft aus, Dauer 5 Sekunden

Sofern nicht anders angegeben, beträgt die Montagehöhe von
Lichtschaltern 1,05 Meter über Oberkante Fertigfußboden (OKFF)
und die Montagehöhe von Steckdosen 0,3 Meter über Oberkante
Fertigfußboden (OKFF).
Alle Maße sind bauseits auf Einhaltung der relevanten Normen und
Richtlinien (insbesondere DIN 18015 und DIN VDE 0100) zu prüfen und anzupassen.

Legende	
	KNX Decken-Präsenzmelder
	Rettungszeichen-Leuchte in DS, Pilotprogramm rechts einseitig
	Rettungszeichen-Leuchte in DS, Pilotprogramm geradeaus
	Sicherheits-Leuchte für Deckenmontage in BS
	Sicherheits-Leuchte für Wandmontage in BS
	Hinweisleuchte "Feuertürschloß"
	LED-Einbau-Leuchte, eckig
	LED-Einbau-Strahler, rund/für
	LED-Einbau-Raster-Leuchte, eckig
	Aufbauleuchte FR IP43, rund NWC
	Spiegelleuchte Kristall
	LED-Anbau-Pendel-Leuchte, eckig
	LED-Anbau-Leuchte, eckig
	Wandauslass für Leuchtenanschluss
	Deckenauslass für Leuchtenanschluss
	LED-Einbau-Strahler, rund
	LED-Pendelleuchte, rund/für NG
	BMA Notstrommelder (GND+MND+HMD) (OTT)
	BMA Nichtautomatischer Melder, rot (NAM)
	BMA Signalleuchte, akustisch (SA)
	BMA Signalleuchte, optisch (SO)
	BMA Feuerwarn-Schmelzdepot (FSD)
	BMA Feuerwarn-Zentrale (FZ)
	Revisionsklappe 0,60m x 0,60m
	VS Video-Netzwerkamera
	ERM Umschalt-Bewegungsmelder (UM)
	ZK elektronischer Türöffner (TF)
	RWA Lüfterstator
	BMA Anzeigetafelbau AT
	Elektrischer Anschluss
	Brandschutzklappe mit LV Pse. 1.6.1.10
	Rolladenknieb 230V
	Schaltdose H=1,40 als Reserve für Thermostat, inkl. M20 Lüfter bis in Abhängigkeit
	Potentiaausgleichslehne 4 Anschlüsse
	Kabelrinne, verschiedene Breiten
	Stützgrasse leichte, Höhe 60 mm, Breite 300 mm
	UP Taster mit Neutralisator
	UP Ausschalter
	UP Jalousieventilator/Taster
	AP Taster
	UP Schliesseinschalter 1-pol.
	UP Tür Auslöserstator
	UP Schloßketteleiste
	UP CEE-Anbauketteleiste 32A
	Wandspare/Telefonboxe
	Daten-Anschlußdose Cat.7 1x R345 UP
	Daten-Anschlußdose Cat.7 1x R345 UP
	ELA Lautsprecher Decke
	ELA Lautsprecher im Gehäuse
	ELA Mikrophon
	BMA Notstrommelder (GND+MND+HMD) (OTT)
	System-Haustelefon, Comfort
	Zimmer-Signalleuchte 4 Kammern
	Zugtaster mit Schmir und Knopf
	Ruf- und Abhörtaster
	Abhörtaster
	KNX Mintabau
	KNX Tastensor 1-fach
	KNX Tastensor 2-fach
	KNX Dimm/Jalousie-Tastensor
	KNX Taster-Schaltstelle
	Ventilatorschrank
	Netzwerkschrank
	Brüstungsbalken, Höhe 70mm x Breite 130mm
	Sockelleistenkanal, Höhe 20mm x Breite 70mm
	Übergabeboden für Sonnenschutz

20250917-2220-EG-E-M50

B1487 x H1050



Elektrotechnik Hebrock GmbH
Am Haubach 4 32584 Löhne
Tel: 05732 / 98 33 888
Email: info@elektro-hebrock.de

Montage und Werkplan

18.09.2025
Druck-Datum

ABO
gezeichnet

geprüft

1:50
Maßstab

Blatt
1 von 1